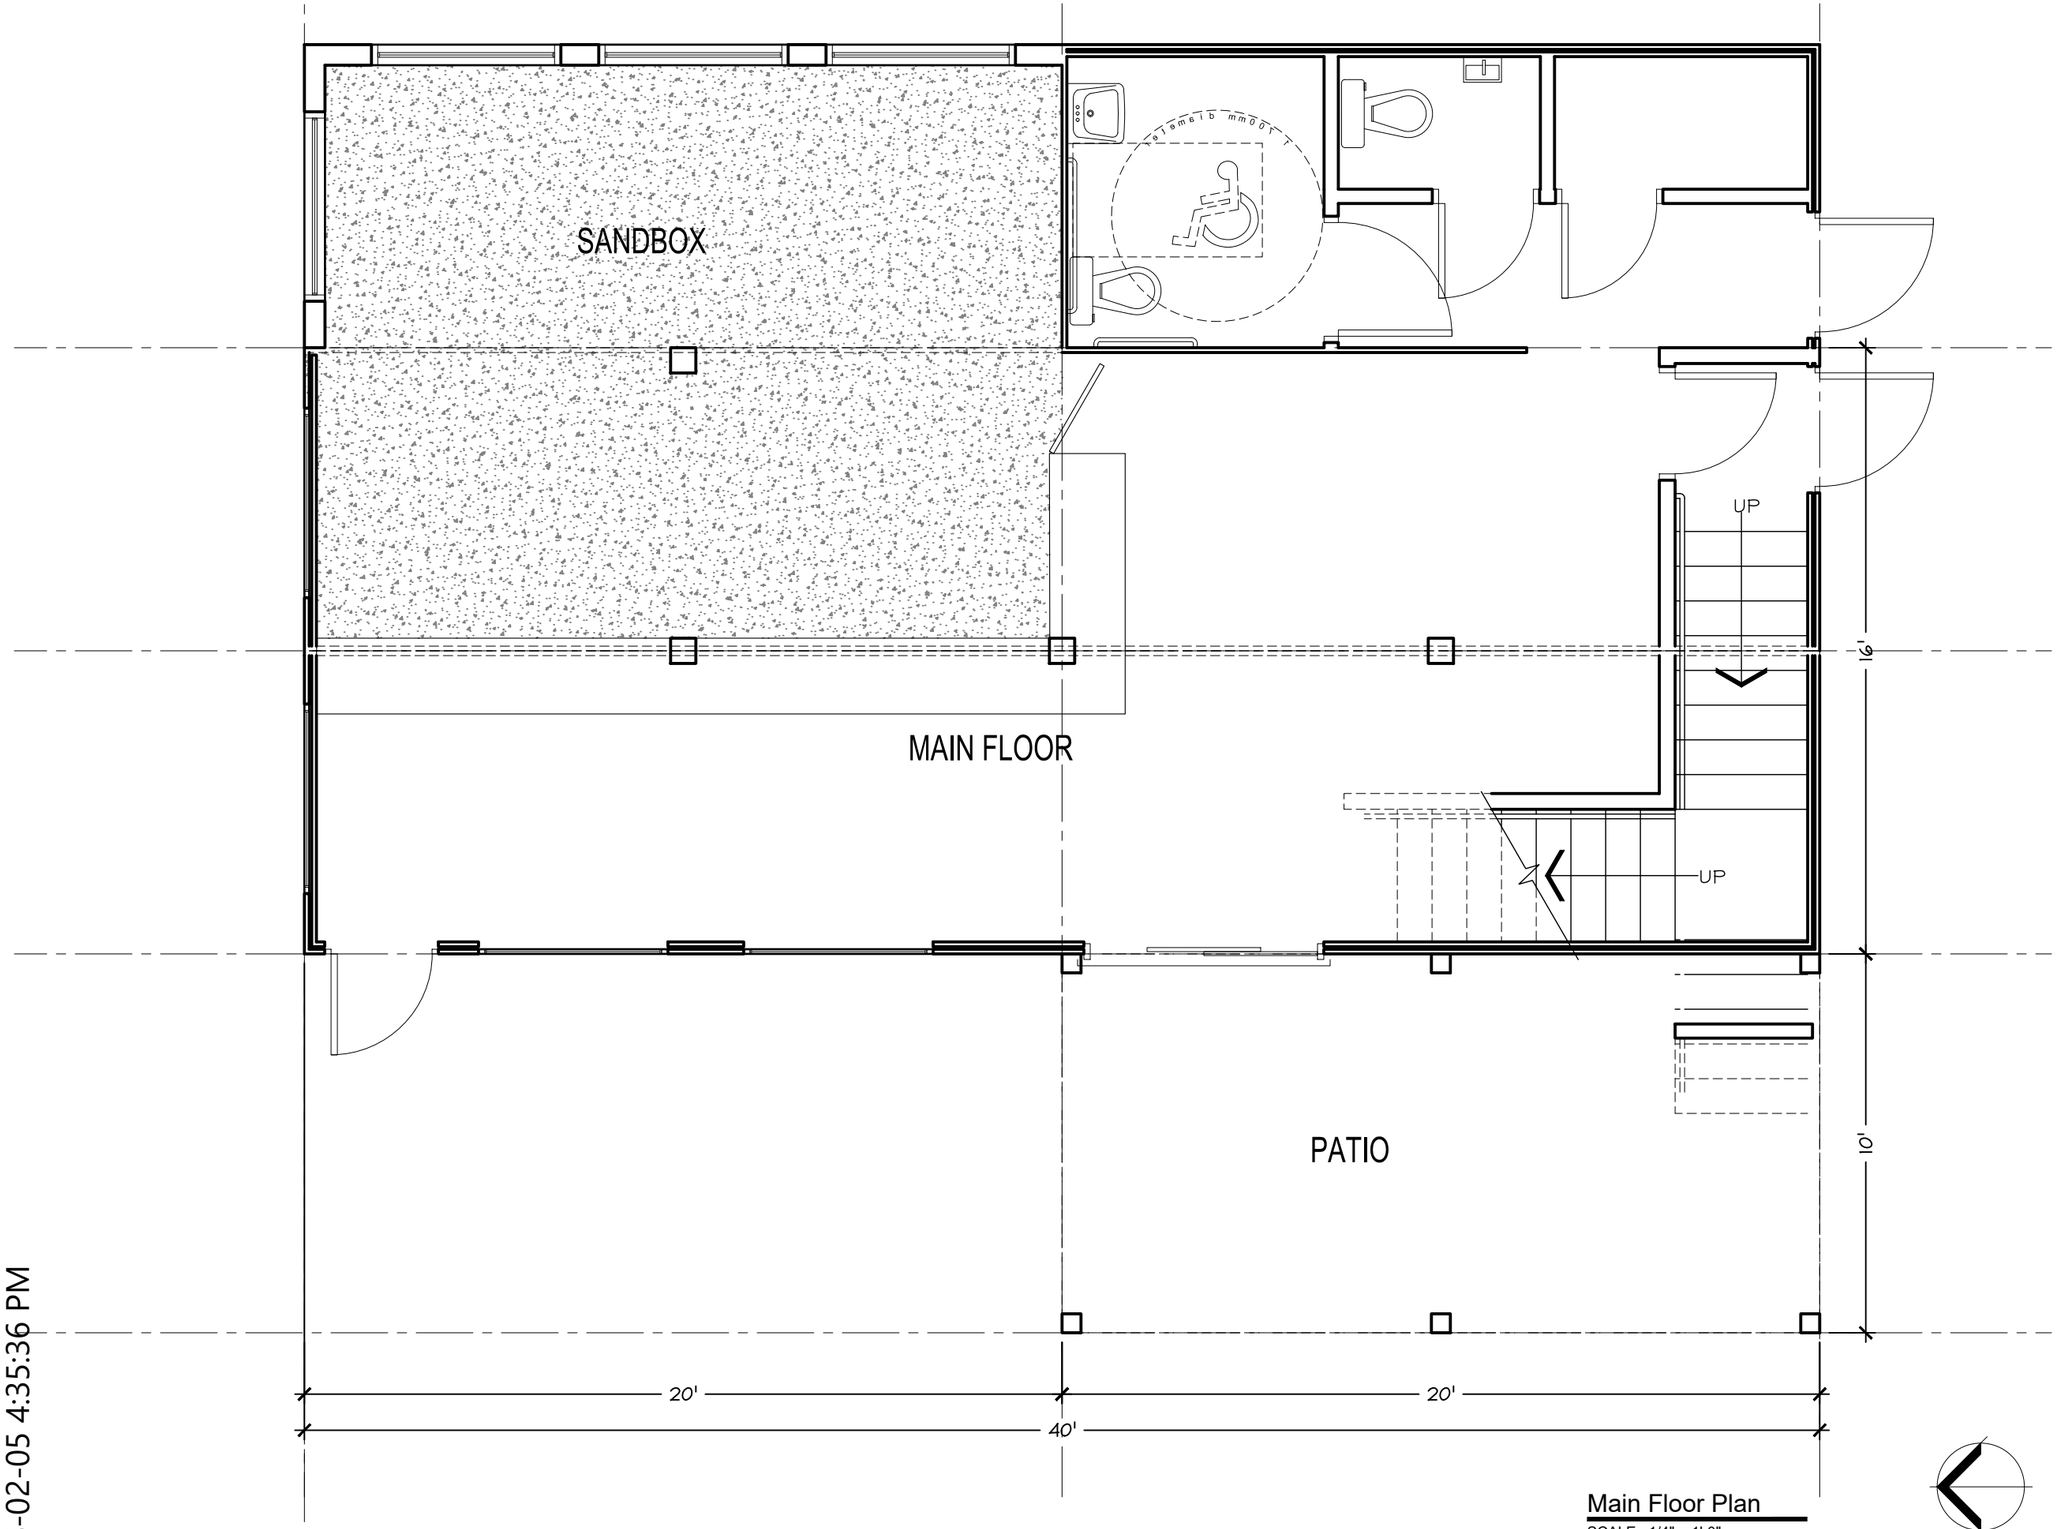

Main Floor Plan

SCALE : 1/4" = 1'-0"

jacquelyn skeffington

KOKANEE CAFE
DIGGER CAFE
KOKANEE CAMPGROUND
SEBA BEACH, ALBERTA

MAIN FLOOR PLAN

january 2026
job no. 4067
a10.1

edmonton
canada
780.455.3590

2026-02-05 4:35:36 PM

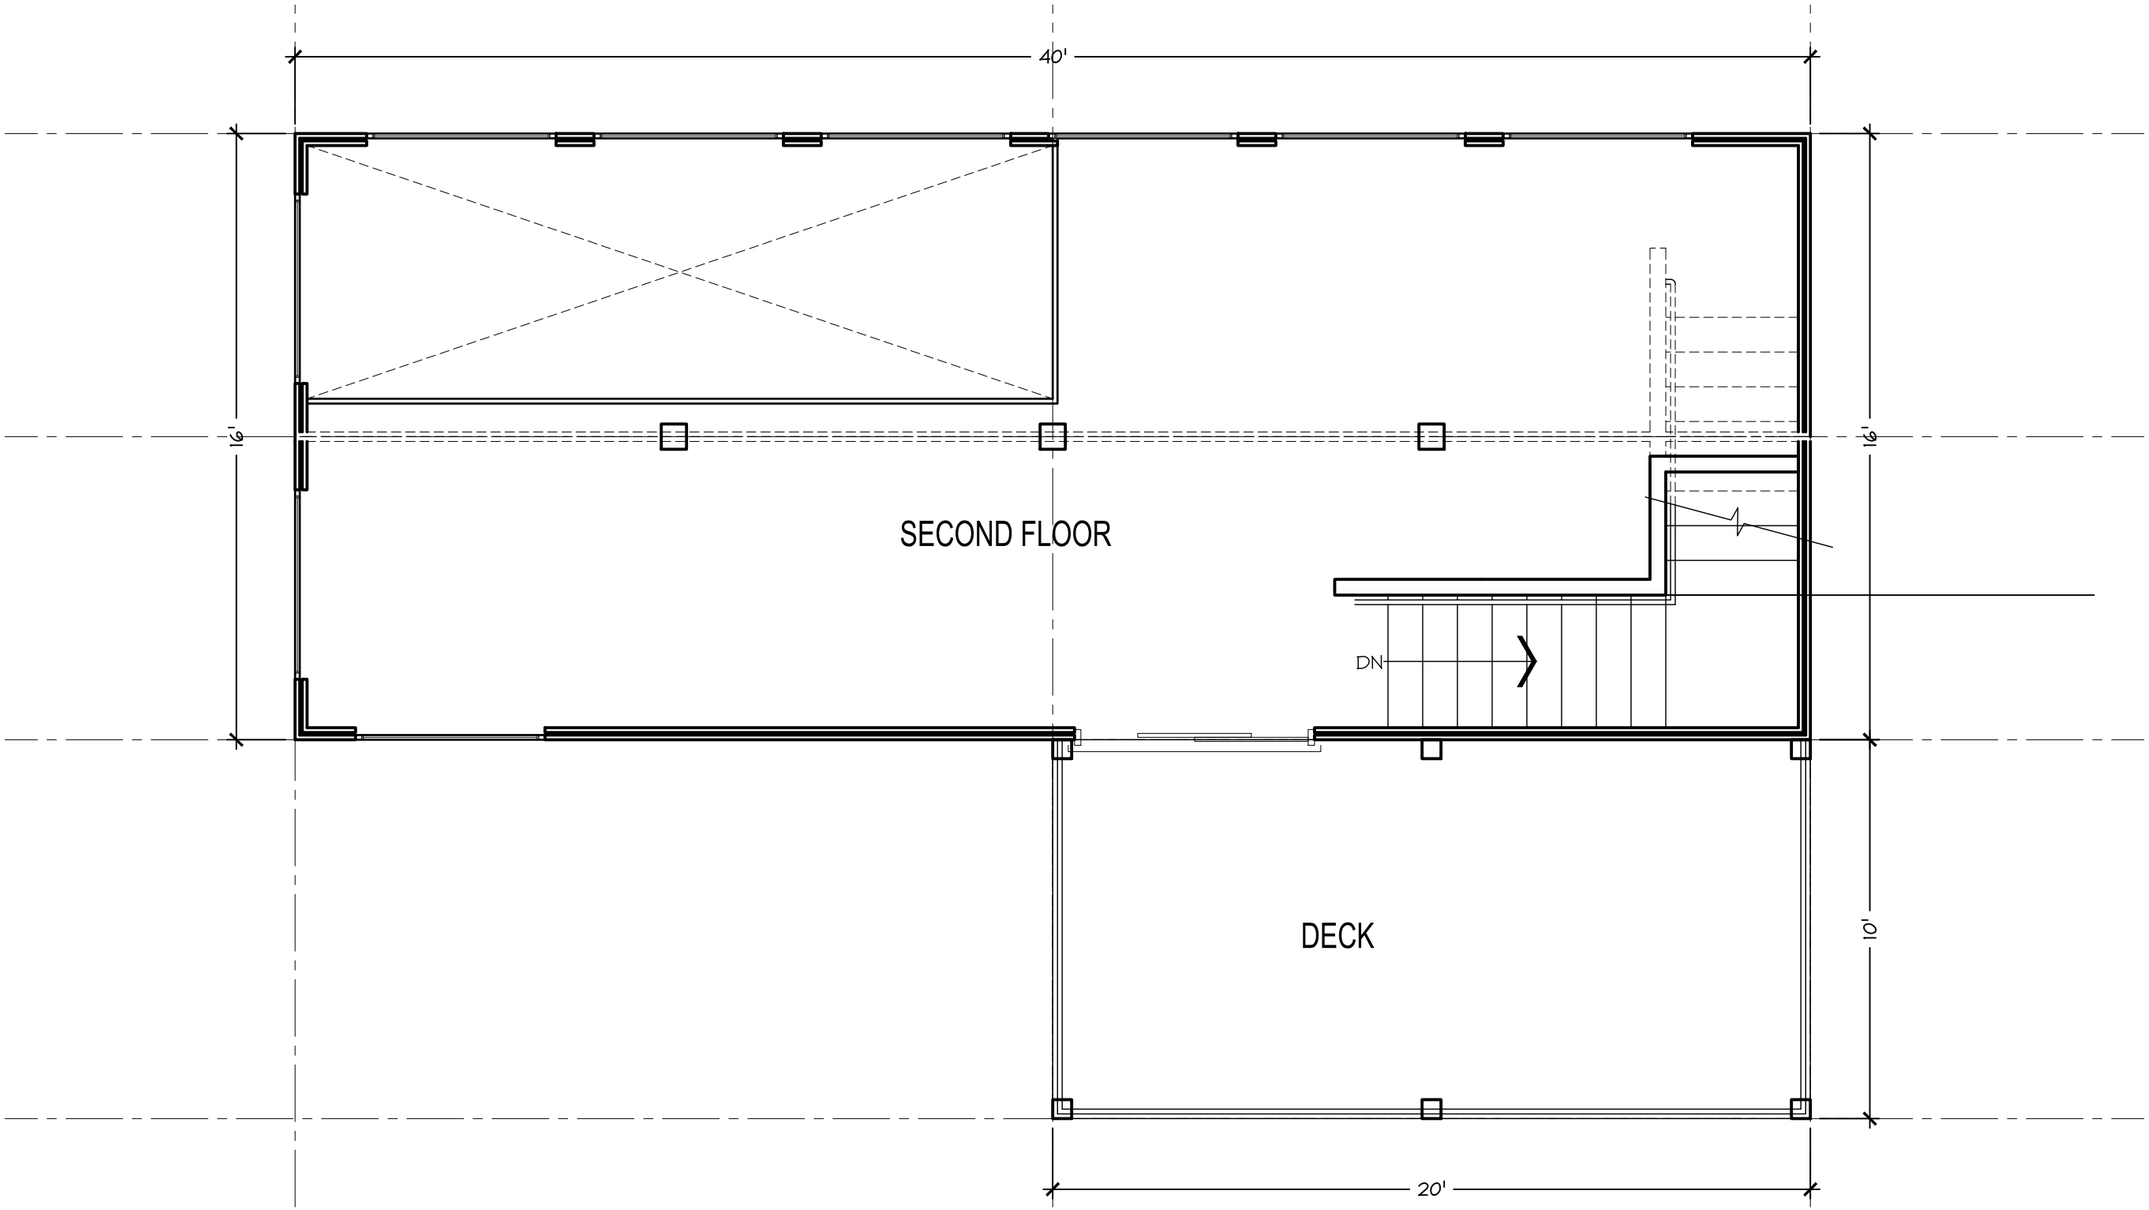

Second Floor Plan

SCALE : 1/4" = 1'-0"

jacquelyn skeffington

NORTH

KOKANEE CAFE
DIGGER CAFE
KOKANEE CAMPGROUND
SEBA BEACH, ALBERTA

SECOND FLOOR PLAN

january 2026
job no. 4067
a10.2

edmonton
canada
780.455.3590

2026-02-05 4:35:37 PM

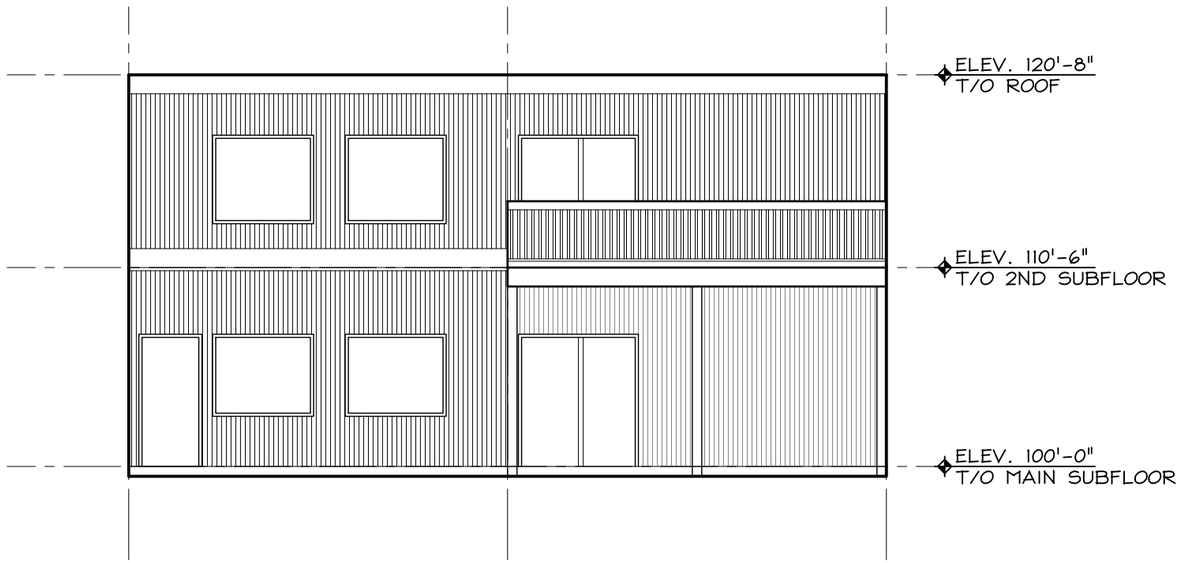

West Elevation
SCALE : 1/8" = 1'-0"

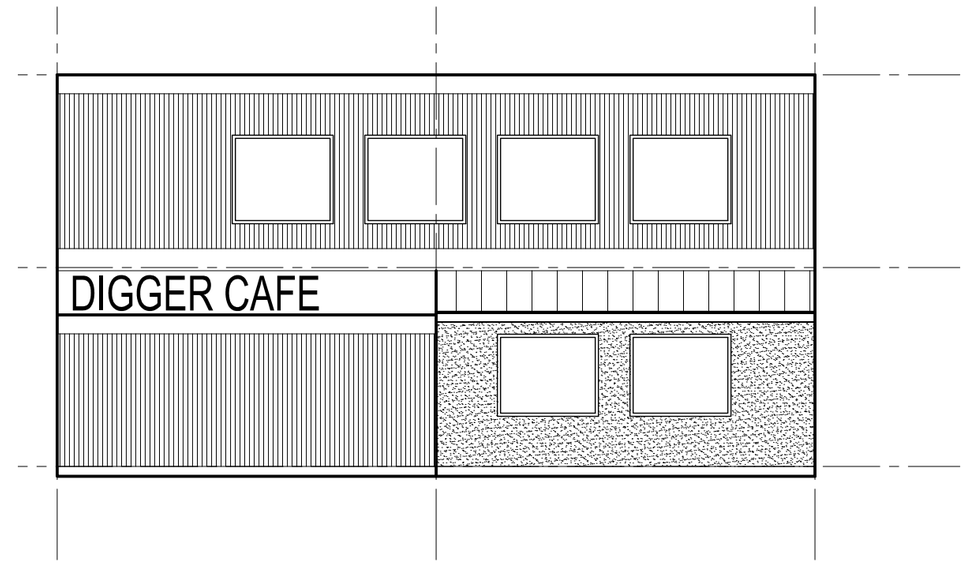

East Elevation
SCALE : 1/8" = 1'-0"

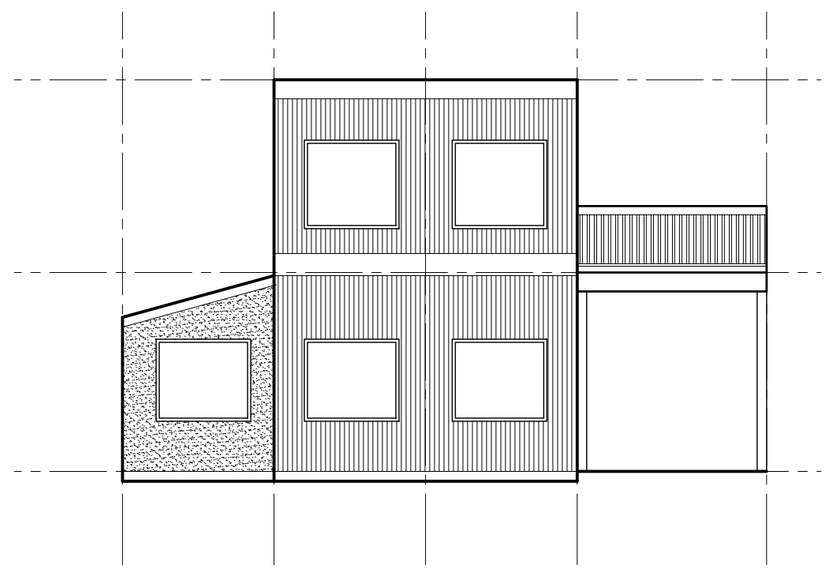

North Elevation
SCALE : 1/8" = 1'-0"

jacquelyn skeffington

KOKANEE CAFE
DIGGER CAFE
KOKANEE CAMPGROUND
SEBA BEACH, ALBERTA

january 2026
job no. 4067
a20.1

edmonton
canada
780.455.3590

ELEVATIONS

2026-02-05 4:35:37 PM