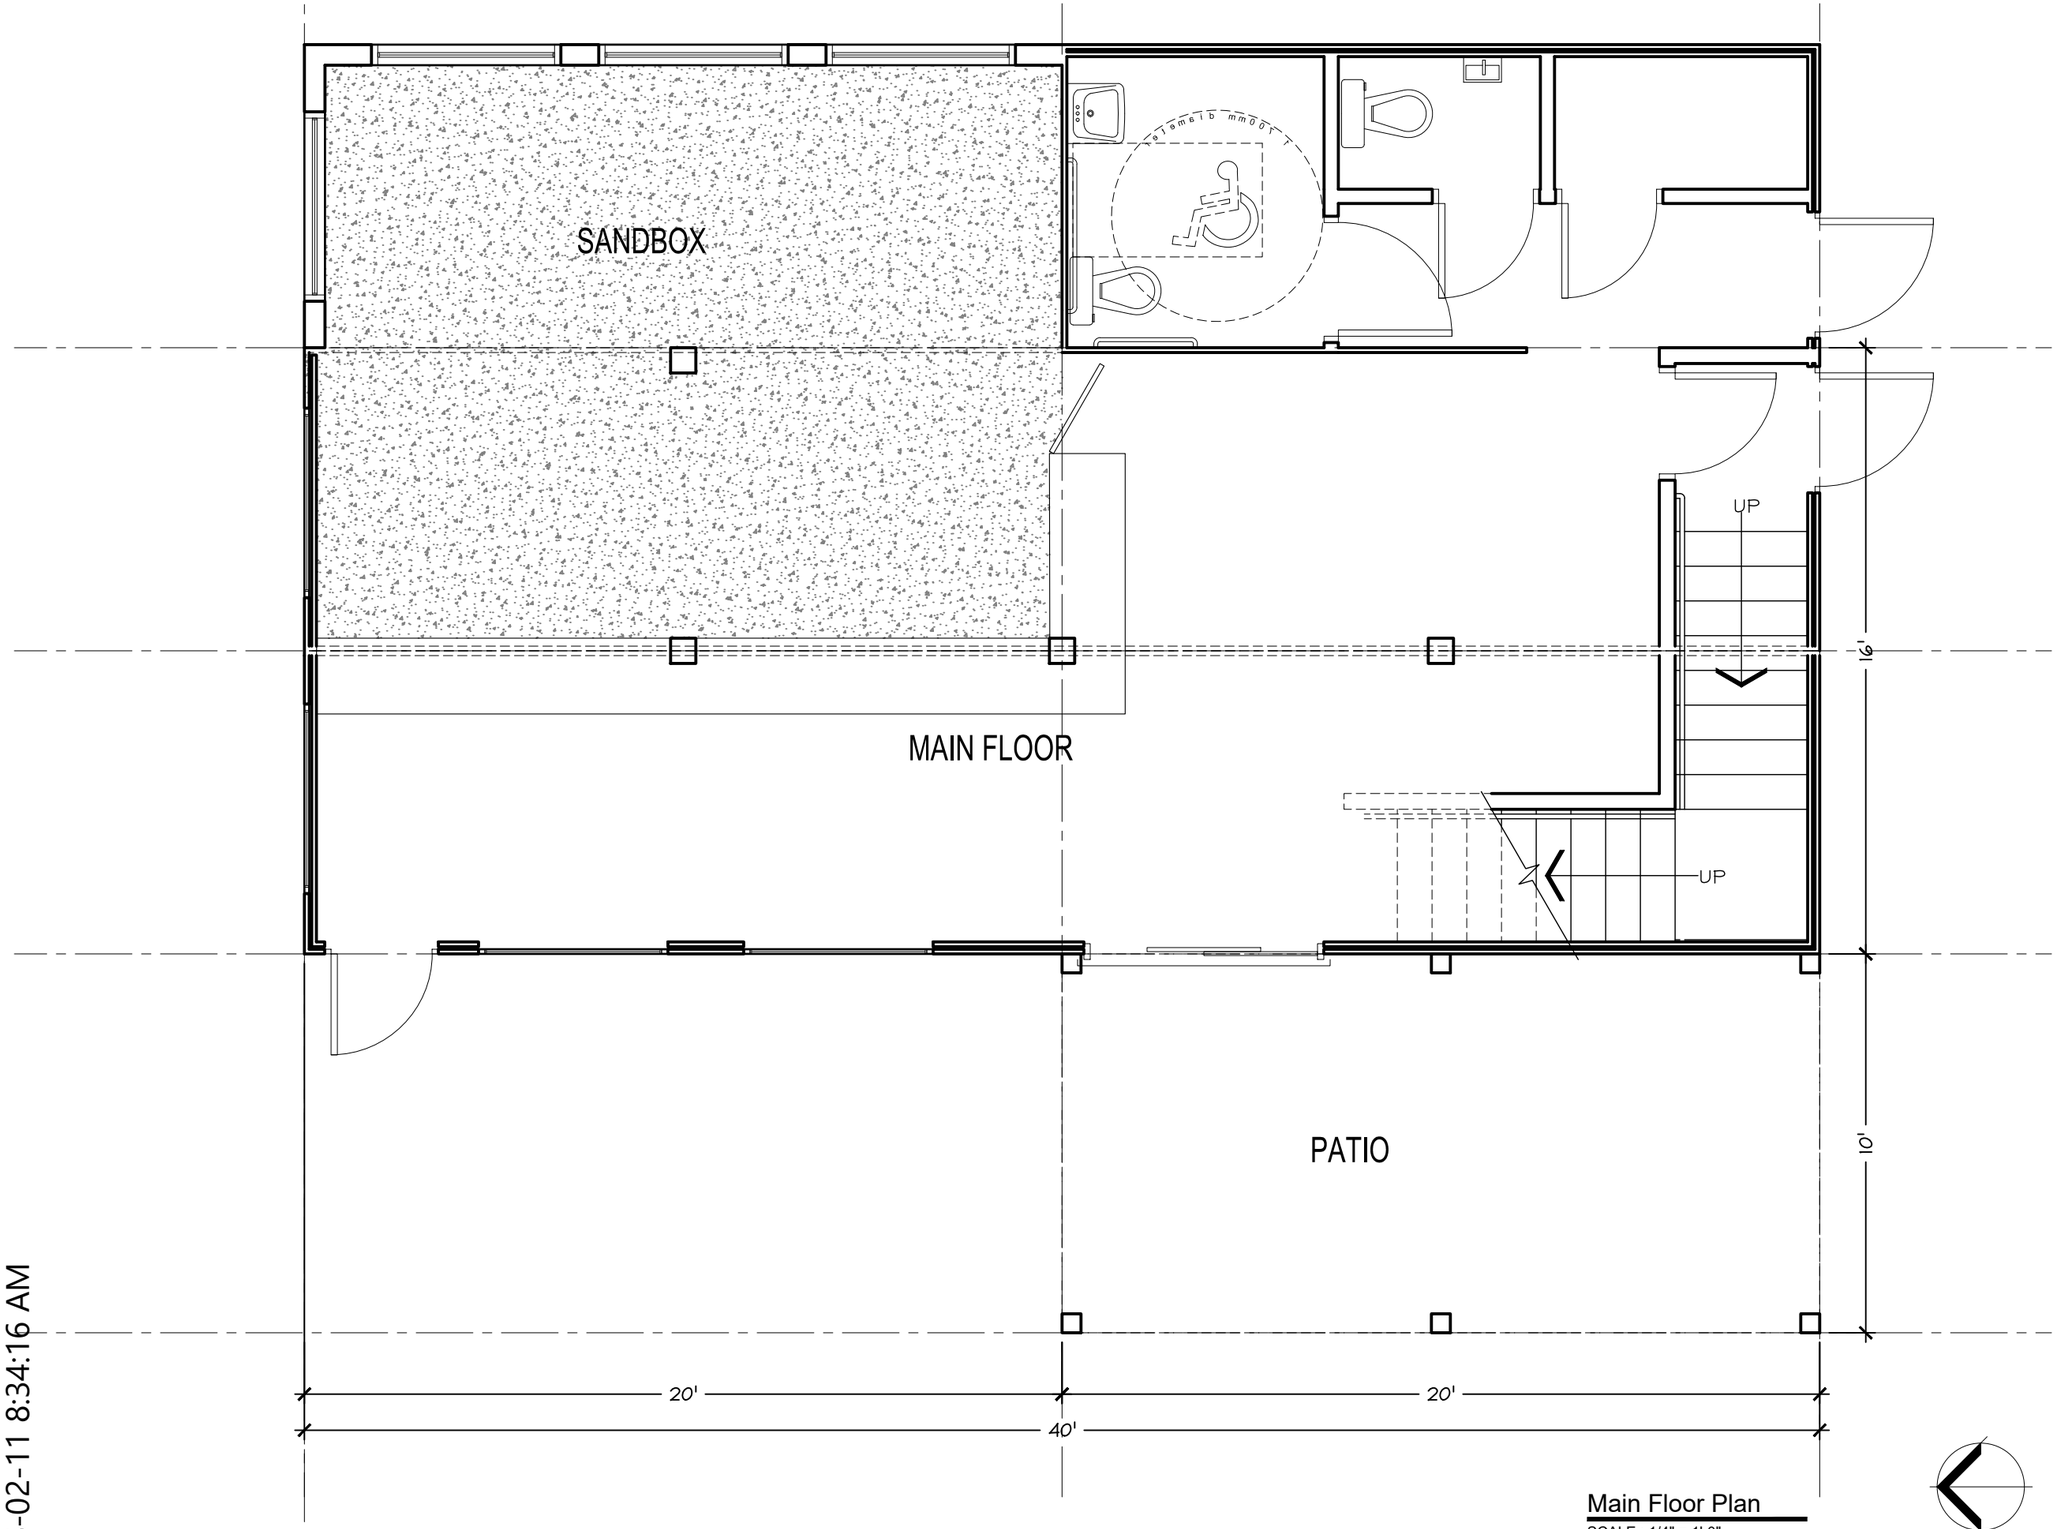


Main Floor Plan

SCALE : 1/4" = 1'-0"

jacquelyn skeffington

KOKANEE CAFE
DIGGER CAFE
KOKANEE CAMPGROUND
SEBA BEACH, ALBERTA

MAIN FLOOR PLAN

january 2026
job no. 4067
a10.1

edmonton
canada
780.455.3590

2026-02-11 8:34:16 AM

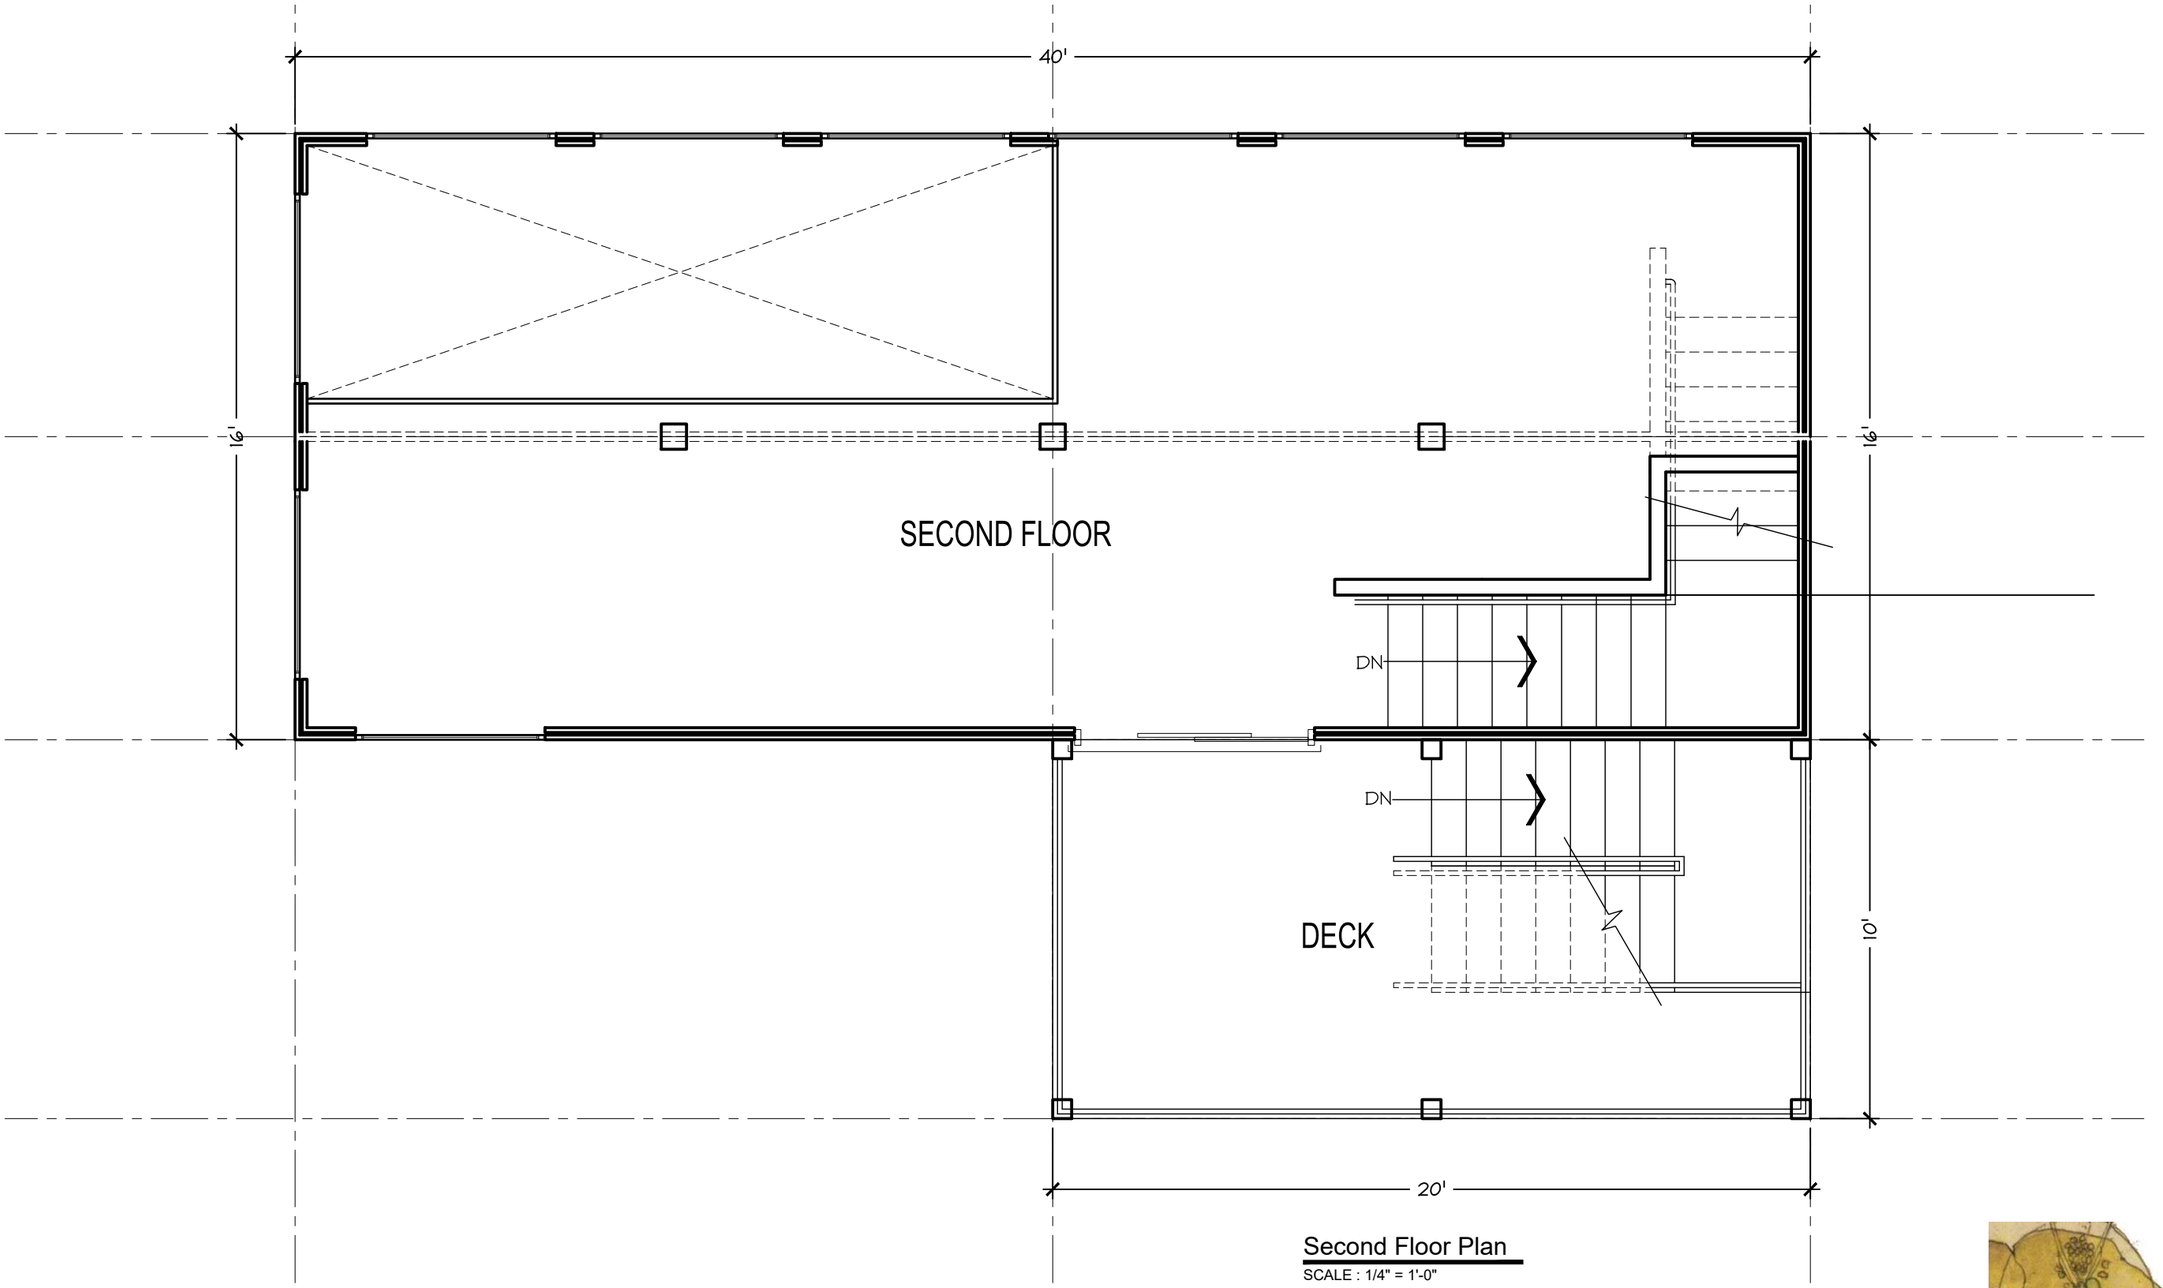


Second Floor Plan

SCALE : 1/4" = 1'-0"

jacquelyn skeffington

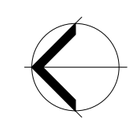


KOKANEE CAFE
DIGGER CAFE
KOKANEE CAMPGROUND
SEBA BEACH, ALBERTA

SECOND FLOOR PLAN

january 2026
job no. 4067
a10.2

edmonton
canada
780.455.3590

2026-02-11 8:34:16 AM

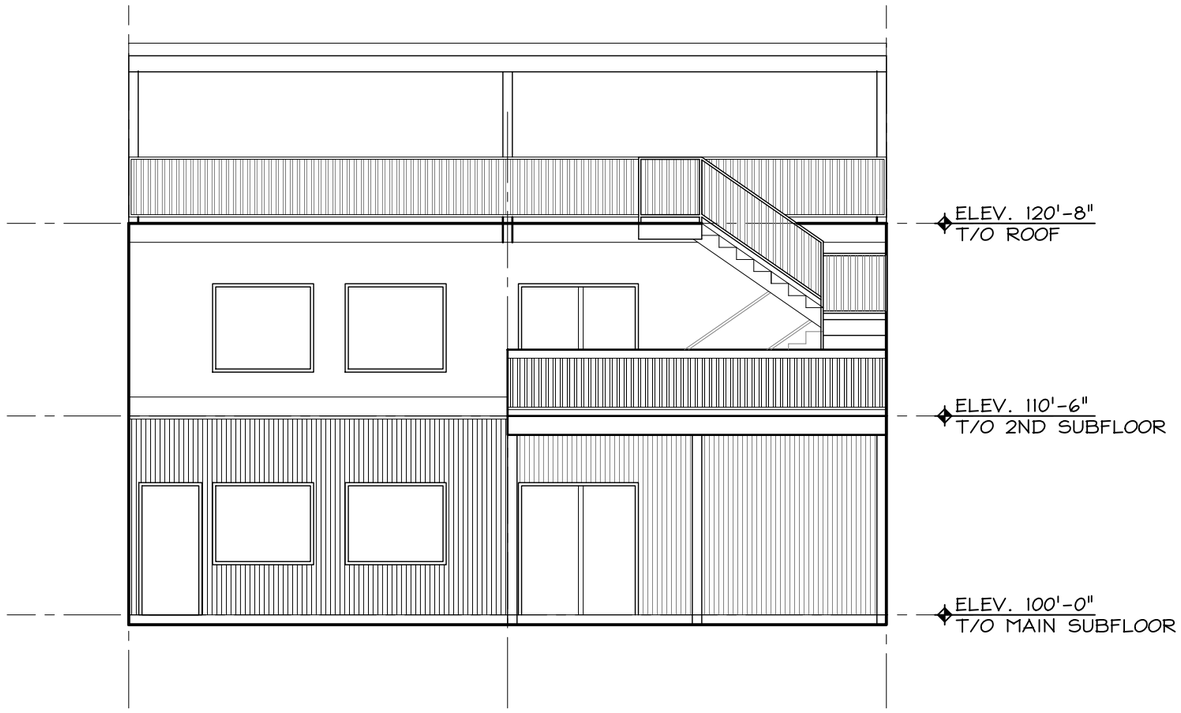


West Elevation

SCALE : 1/8" = 1'-0"

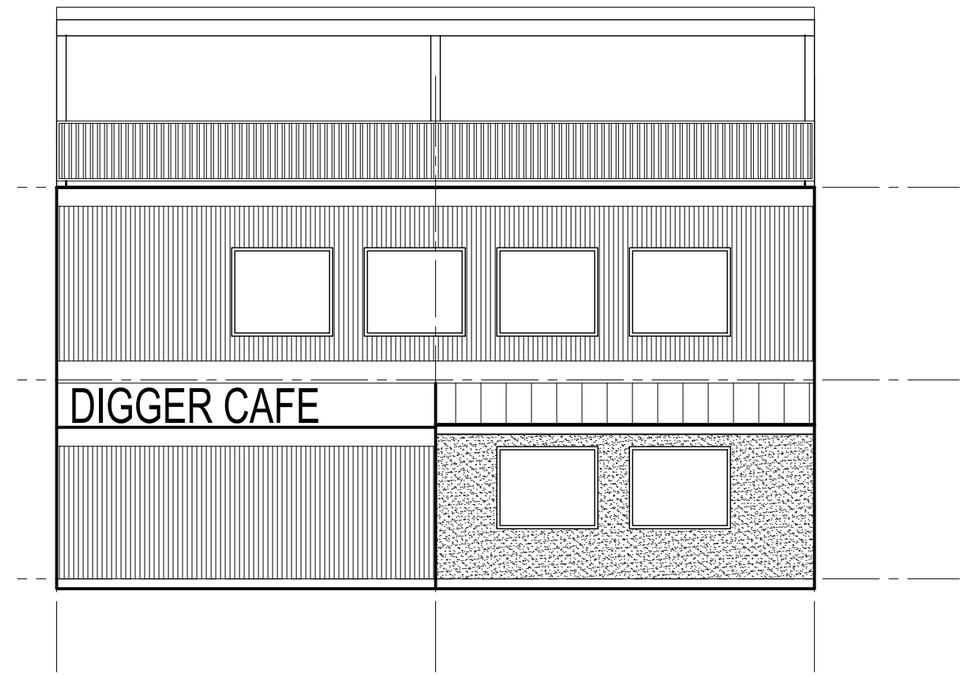


East Elevation

SCALE : 1/8" = 1'-0"

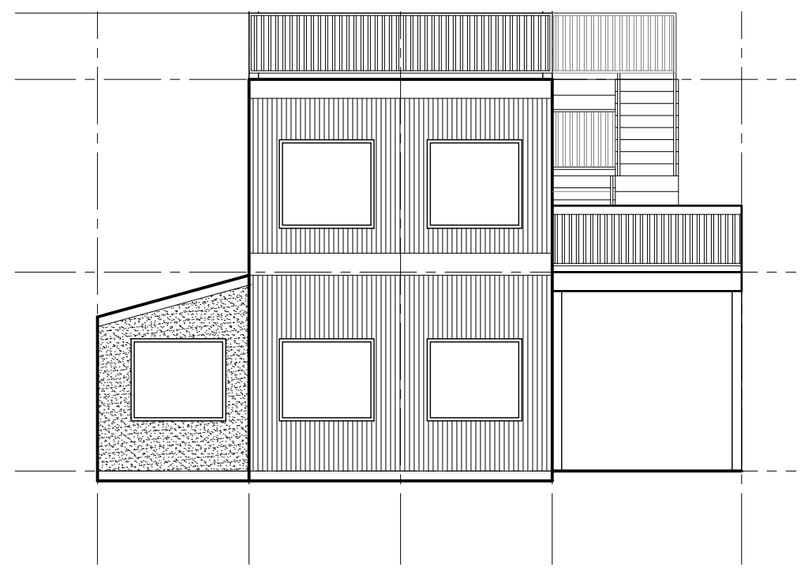

North Elevation

SCALE : 1/8" = 1'-0"

2026-02-11 8:34:16 AM

jacquelyn skeffington

KOKANEE CAFE
DIGGER CAFE
KOKANEE CAMPGROUND
SEBA BEACH, ALBERTA

ELEVATIONS

january 2026
job no. 4067
a20.1

edmonton
canada
780.455.3590